


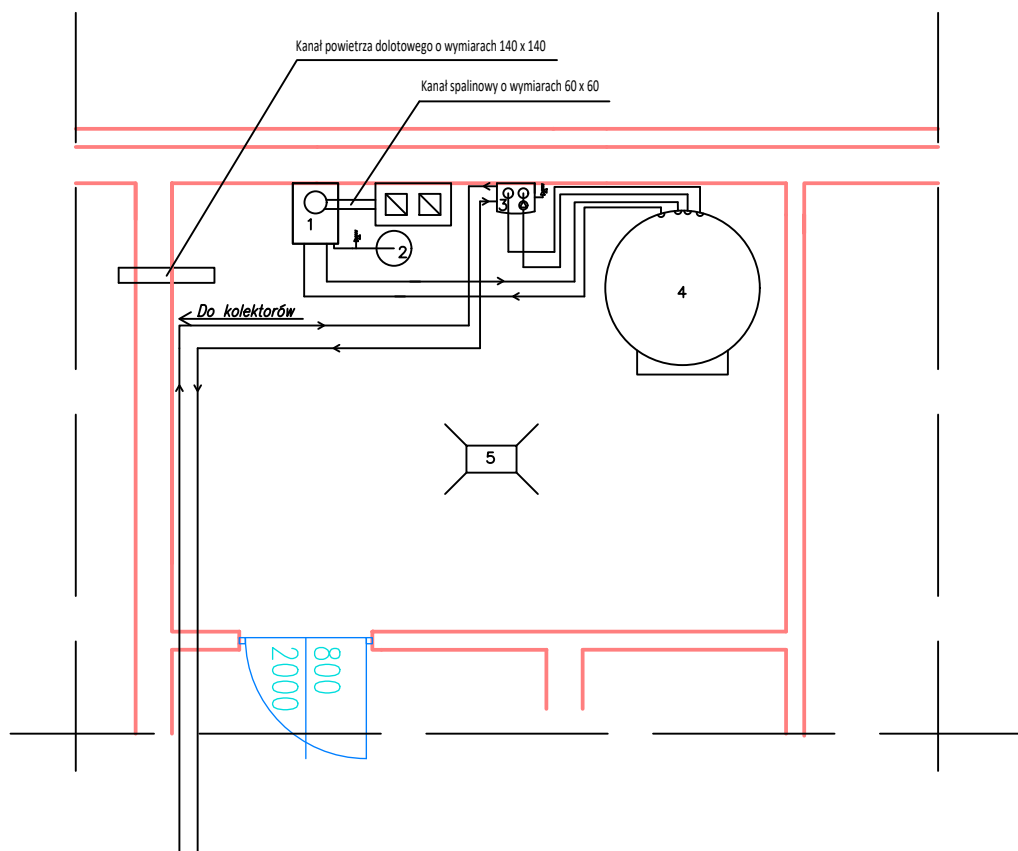

### Legenda:

1. Kocioł na pellet SAS KOT-EFT-017-L-T2, 17 kW.
2. Naczynie wzbiornicze otwarte 25 l.
3. Zestaw pompowy Solar-Divicon typu PS 10.
4. Bufor ciepła Vitocell 300-B, 500 l.
5. Wpust podłogowy.

| Politechnika Lubelska<br>Wydział Inżynierii Środowiska |                               |          |            |
|--------------------------------------------------------|-------------------------------|----------|------------|
| Temat                                                  | Rzut kotłowni wariant 3       | Skala:   | 1:50       |
| Kreślił                                                | Mikita<br>Rymasheuski         | Rysunek: | 4/5        |
| Sprawdziła                                             | dr inż. Anna<br>Musz-Pomorska | Data:    | 17.06.2025 |