


Legenda:

- 1. Kocioł na pellet SAS KOT-EFT-017-L-T2, 17 kW.
- 2. Bufor ciepła Vitocell 300-B, 500 l.
- 3. Zestaw pompowy Solar-Divicon typu PS 10.
- 4. Kolektory słoneczne próżniowe Viessman Vitosol 300 - TM, typ SP3C.

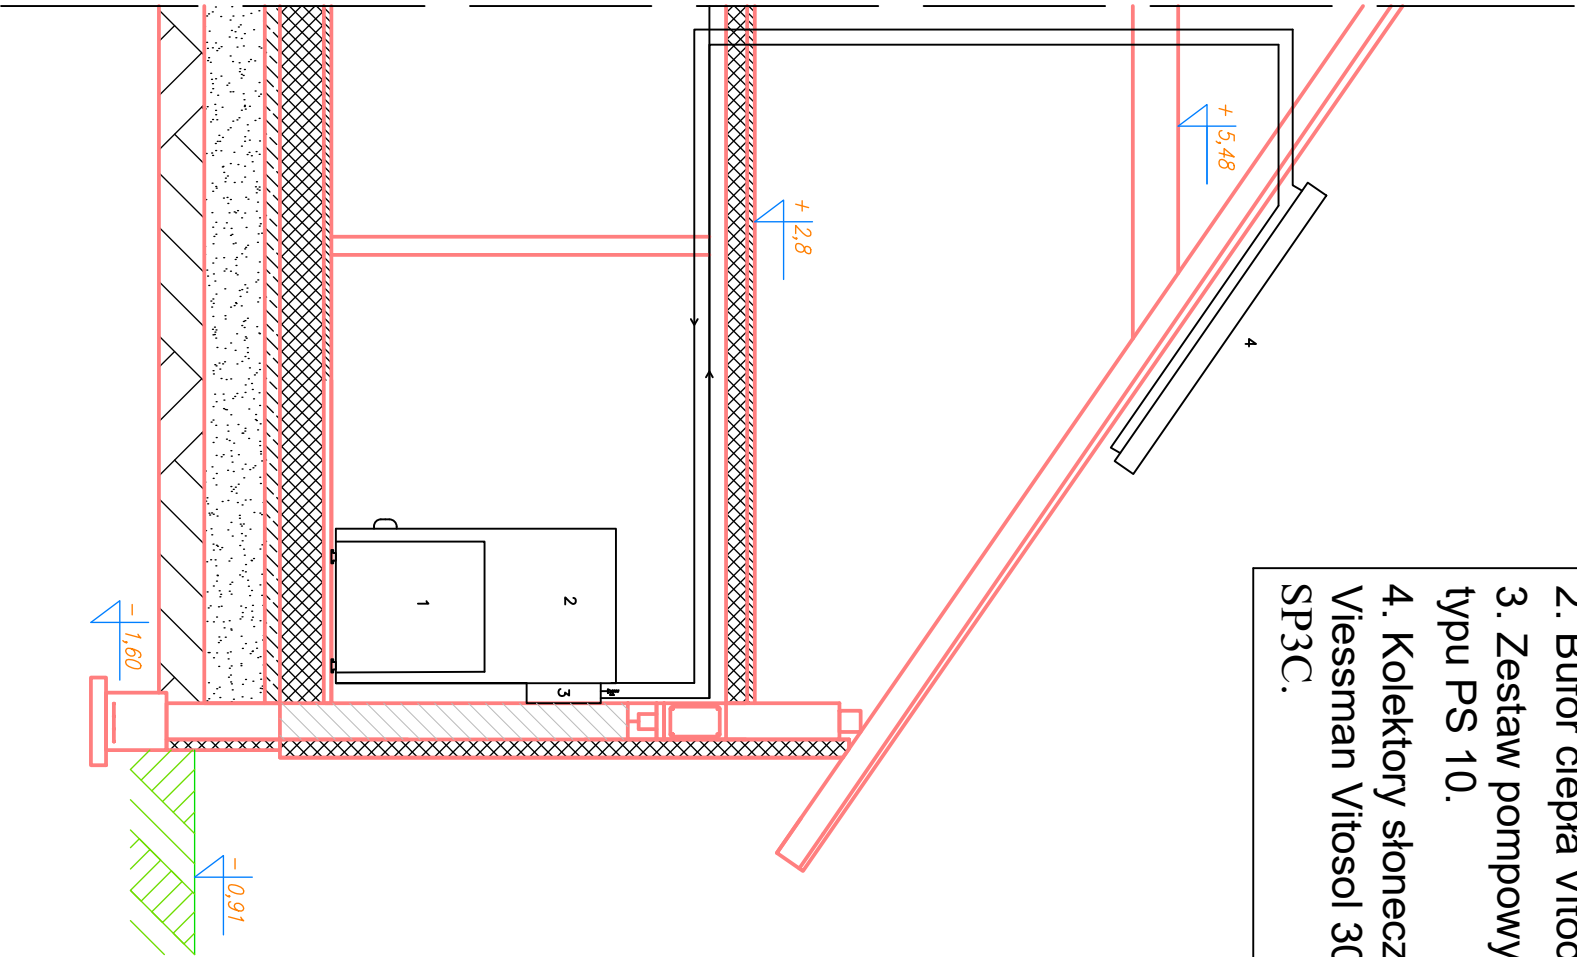

Politechnika Lubelska
Wydział Inżynierii Środowiska

Temat	Przekrój poprzeczny variant 3	Skala:	1:50
Kreślił	Mikita Rymasheuski	Rysunek:	5/5
Sprawdziła	dr inż. Anna Musz – Pomorska	Data:	17.06.2025